




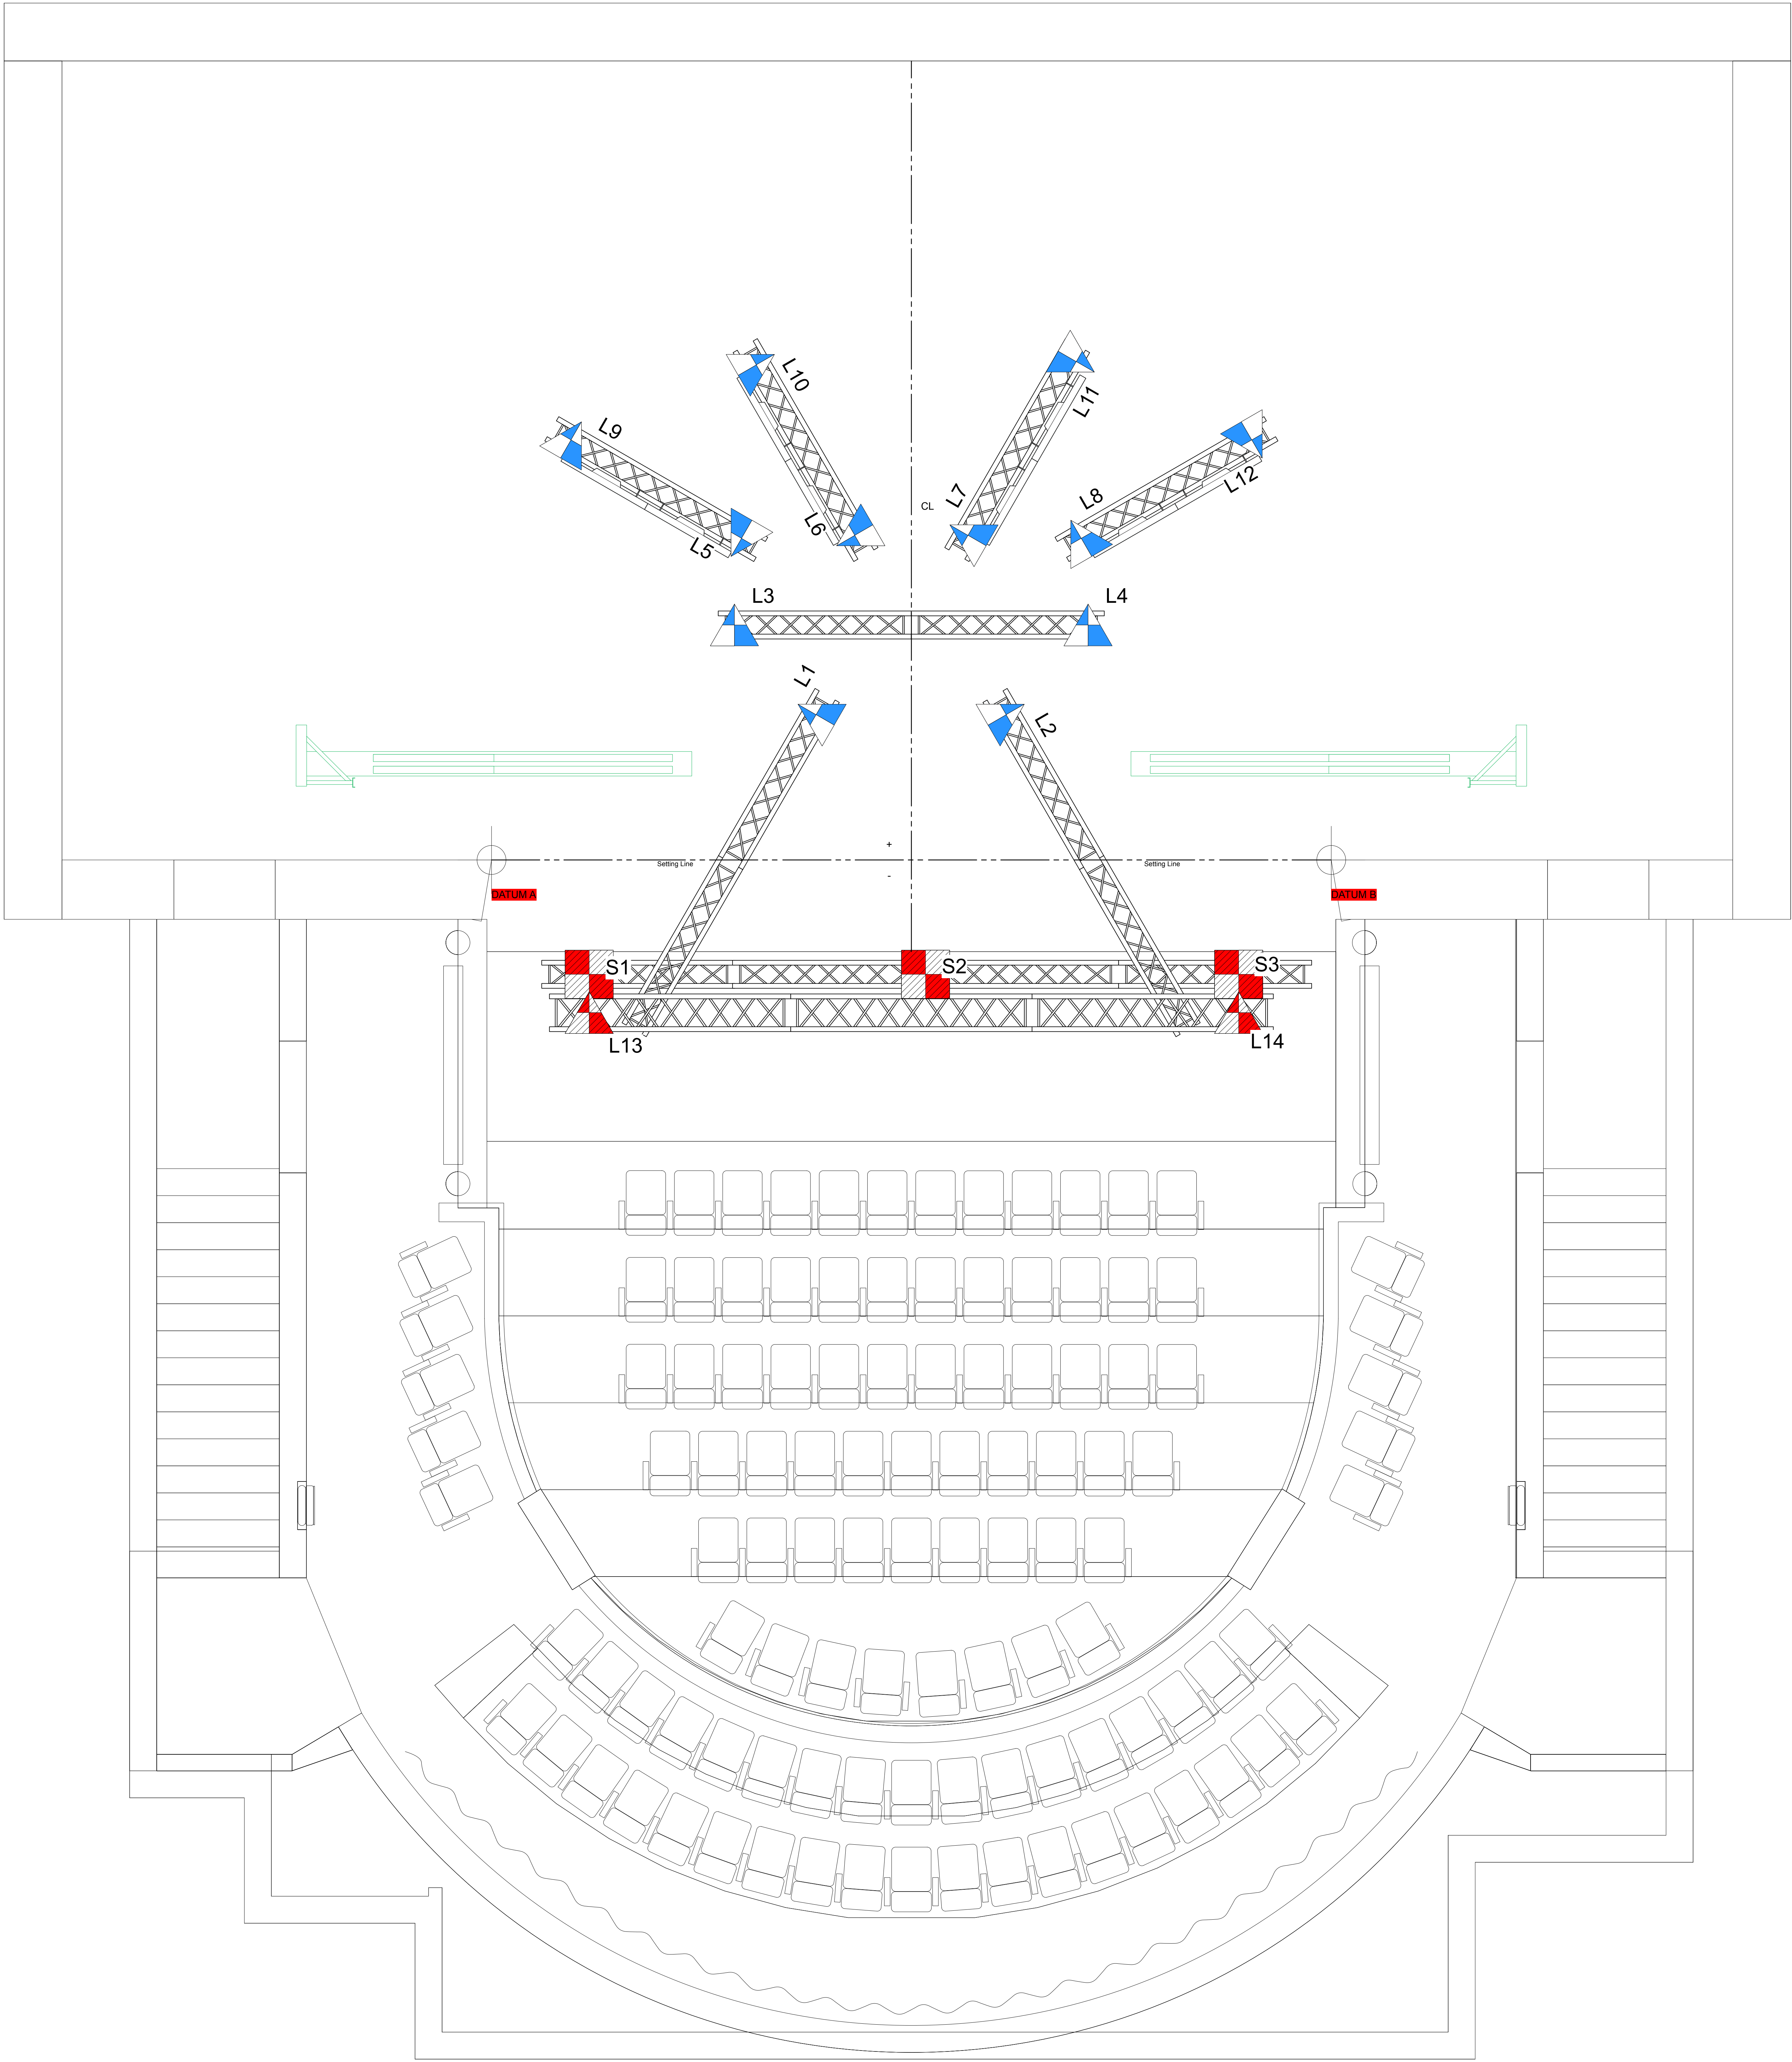


Motor Key

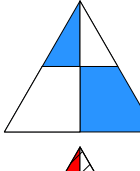

Lighting
500kg Kinesys Elevation

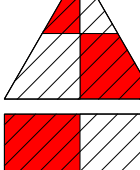

Lighting
1 Ton Lodestar

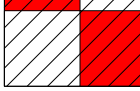

Sound
1 Ton Lodestar



DESIGNED BY Joshua Sanderson		TITLE Fika 'n' Flash	
PHONE NUMBER Joshua Sanderson		Rigging - FOH Points Plan	
Client Sister + Sam and Shamia		DRAWN BY Joshua Sanderson	
Venue Milton Court Theatre		RELATED FILES -	
Address Guildhall School of Music and Drama 1 Milton St, London, EC2Y 8BH		SIZE A0	STATUS CONCEPT
CAD FILE NAME Fika 'n' Flash 9.11.vwx		SCALE 1:25	DATE 07/11/2025
		SHEET 1	OF 6



	DESIGNED BY Joshua Sanderson	Fika 'n' Flash			
	PHONE NUMBER Joshua Sanderson	TITLE Rigging - FOH Elevation			
	CLIENT Sister + Sam and Sharnia	DRAWN BY Joshua Sanderson			
	VENUE Milton Court Theatre	RELATED FILES -			
	ADDRESS Guildhall School of Music and Drama 1 Milton St, London, EX2Y 8BH	SIZE A0	DRAWING NUMBER RIG-2	STATUS CONCEPT	REV A
CAD FILE NAME Fika 'n' Flash 9.11.vwx		SCALE 1:25	DATE 07/11/2025	SHEET 1	OF 6